兴安盟金风科技蒸汽发电节能技术改造项目EPC工程总承包			工程	招标附图	阶段
批 准		设 计		汽轮发电机电气主接线图	
审 核		比 例	/		
		日 期	2026.07		
校 核		版 本	0	图 号	D-01

中国能源建设集团新疆电力设计院有限公司
CHINA ENERGY ENGINEERING GROUP XINJIANG ELECTRIC POWER DESIGN INSTITUTE CO., LTD.

SIZE:A1+1=2A1

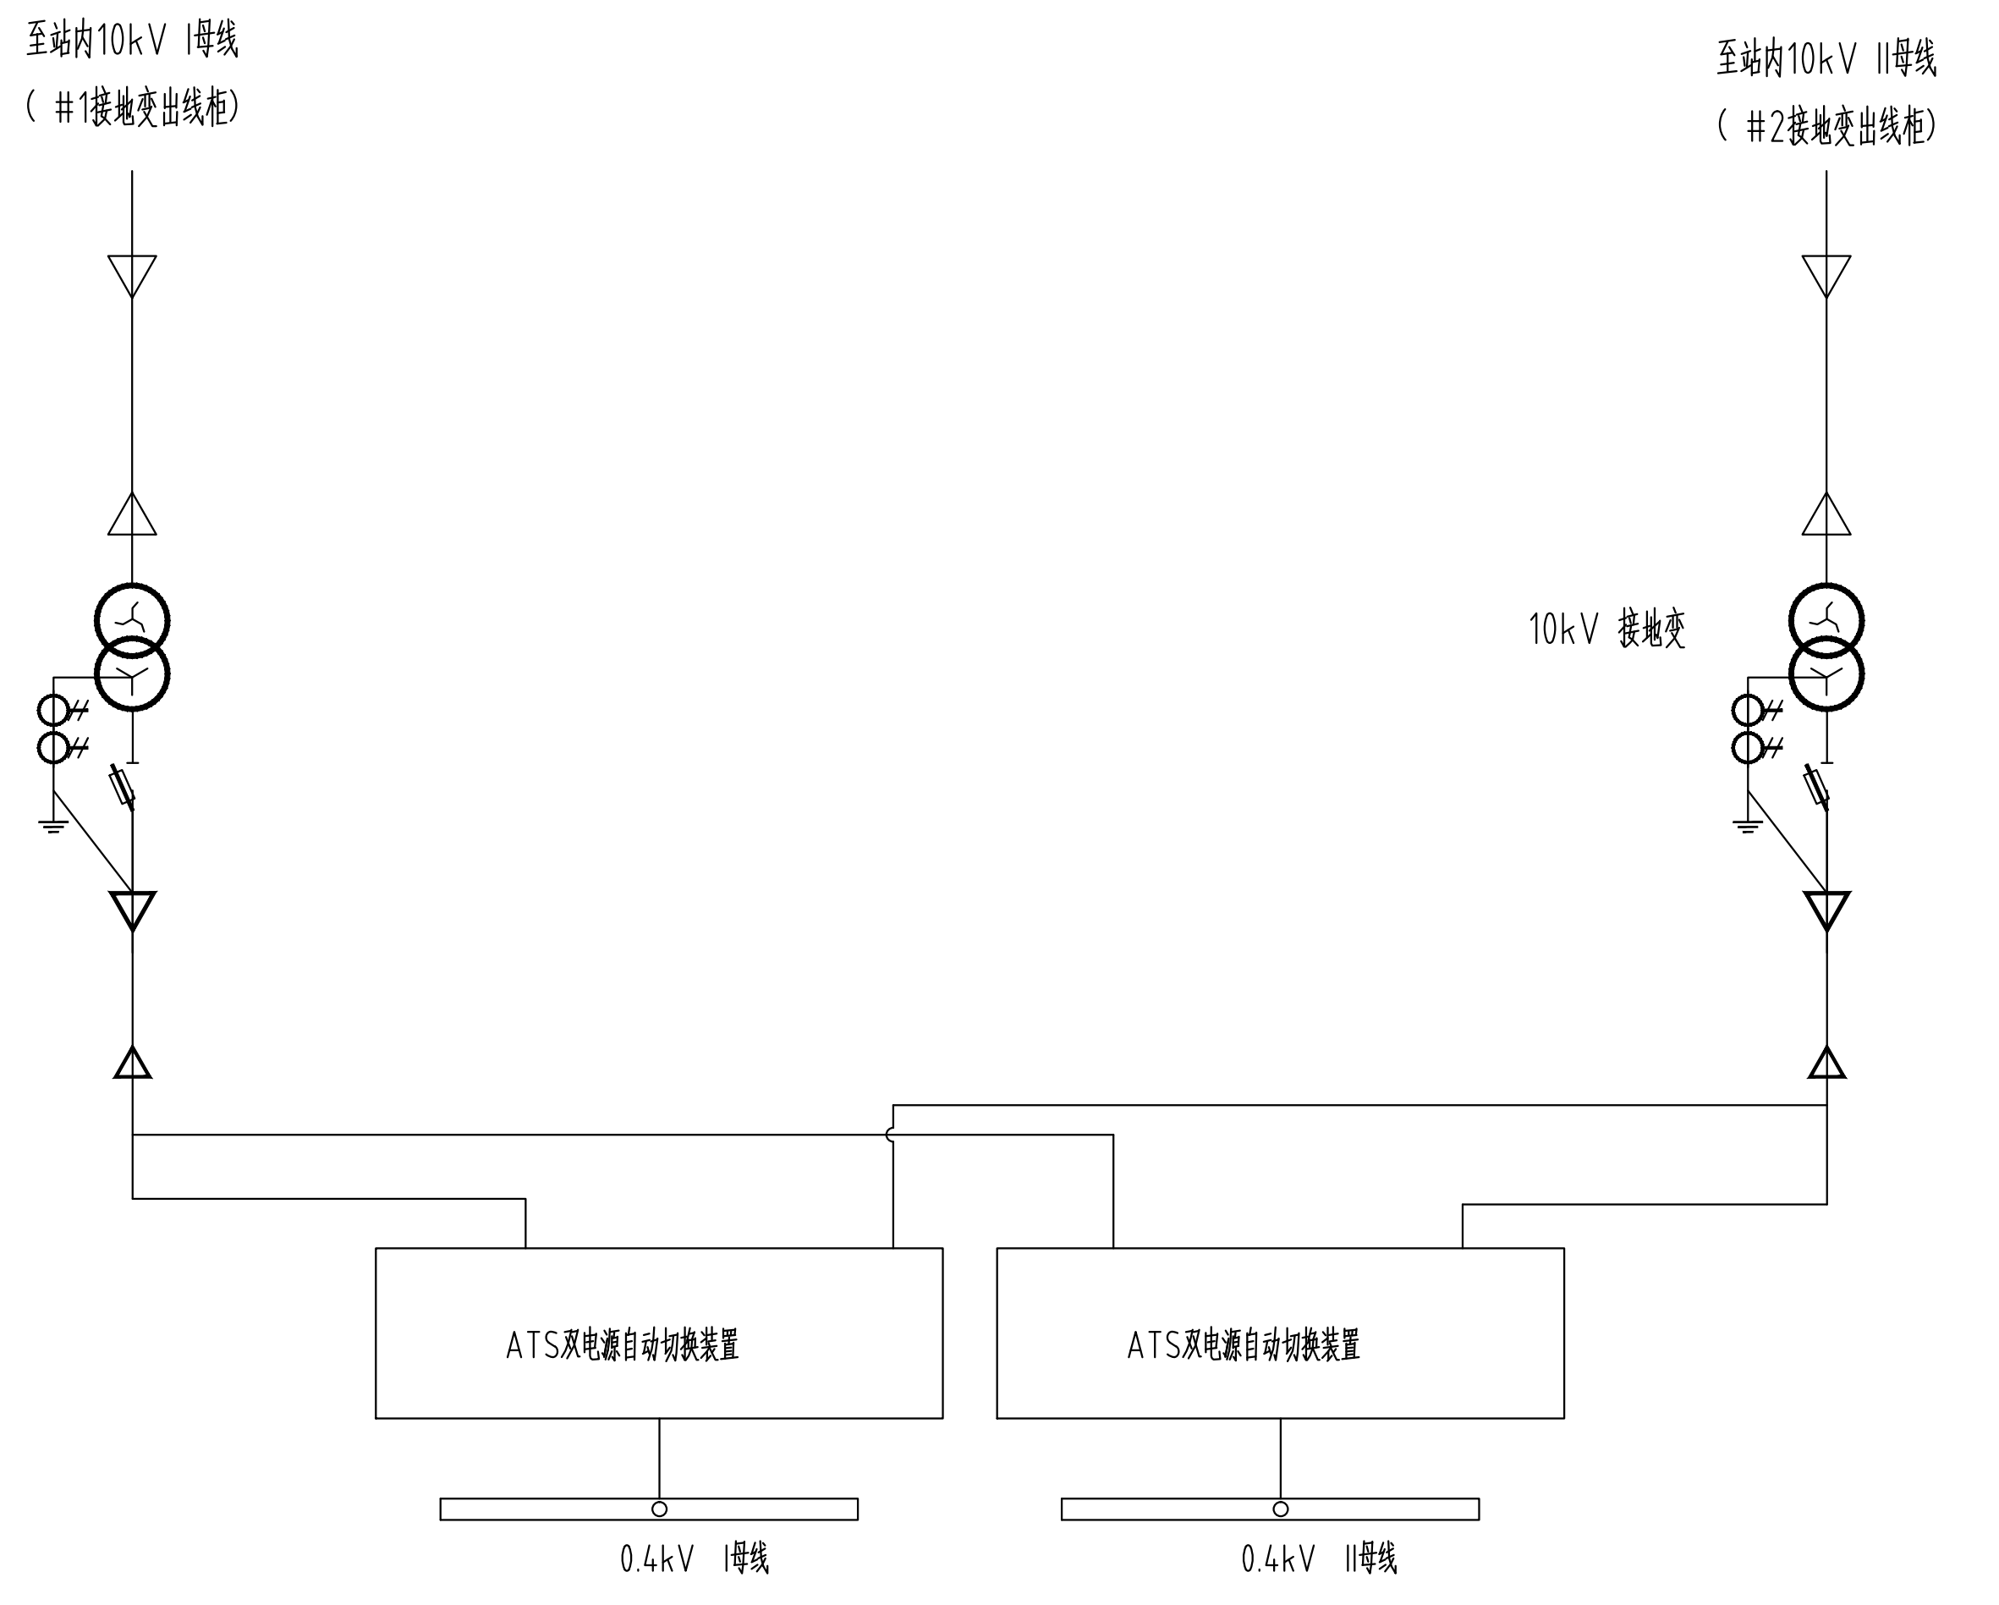

变电站站用电部分接线示意图

1、站用电源配置方案为：设置2台10kV容量为630kVA的接地变,其中站用电容量250kVA。

08
至220kV八连站
07
Ⅱ母设备间隔
电缆进线：ZC-YJLW03-50/66kV-1X1200
（Ixu≈980A，回路工作电流Ig=578.66A）
电缆终端筒 干式470型
电压互感器,附可拆卸导体:
66kV金属氧化物避雷器,附可拆卸导体：Y5WF-96/250
三相带电显示器：126kV（A、B、C）
快速接地开关：126kV 40kA/4S 100kA
三工位隔离接地开关：126kV，2000A 40kA/4S 100kA
电流互感器：600-1200/1A，5P30，15VA
600-1200/1A，0.2S，5VA
断路器：126kV，2000A 40kA/4S 100kA
600-1200/1A，0.5，15VA
ZF39-126，2000A，40kA（4S），100kA
PT(A相)
LA
VD
FES
DES
CT
CB
5P30
0.2S
0.5
电压互感器（A、B、C三相）：
0.2/0.5（3P）/3P/3P，10/50/50/50VA
架空主变进线：JL/G1A-400/35
（Ixu≈696.8A，回路工作电流Ig=643A）
66kV金属氧化物避雷器：YH5W-96/250
SF6/空气套管：126kV，2000A
检修接地开关：126kV，40kA/4S 100kA
Ⅱ母：126kV，2000A，40kA（4S）
2T
1T
主变压器：（配有载调压开关）
满足GB20052-2024中一级能效要求
SZ22-63000/66
开关柜由高压开关柜厂家成套
#1无功补偿成套装置

说明：实线表示已建部分,云线内表示本期工程内容。

说明：

1、66kV变电站规模：

（1）主变压器：终期2X63MVA，本期2X63MVA，主变电压等级66/10.5kV；

（2）66kV出线：终期3回，本期2回；66kV终期及本期采用单母线分段接线。

（3）10kV出线：终期27回，本期22回；终期及本期采用单母线分段接线。

2、无功补偿容量按9.6Mvar 柜式成套无功补偿装置配置。

3、本站站址海拔约280m，电气设备外绝缘不需要海拔修正，空气间隙不需要海拔修正。

4、本期改造新增10kV开关柜2面、限流电抗器2套、原主变端子箱移位、原主变检修箱移位。

兴安盟金风科技蒸汽发电节能技术改造项目EPC工程总承包			工程	招标附图	阶段
批 准		设 计		66kV变电站 电气主接线图（改造后）	
审 核		比 例	/		
		日 期	2026.07		
校 核		版 本	0	图 号	D-02

中国能源建设集团新疆电力设计院有限公司
CHINA ENERGY ENGINEERING GROUP XINJIANG ELECTRIC POWER DESIGN INSTITUTE CO., LTD.

SIZE:A3+0=0.250A1

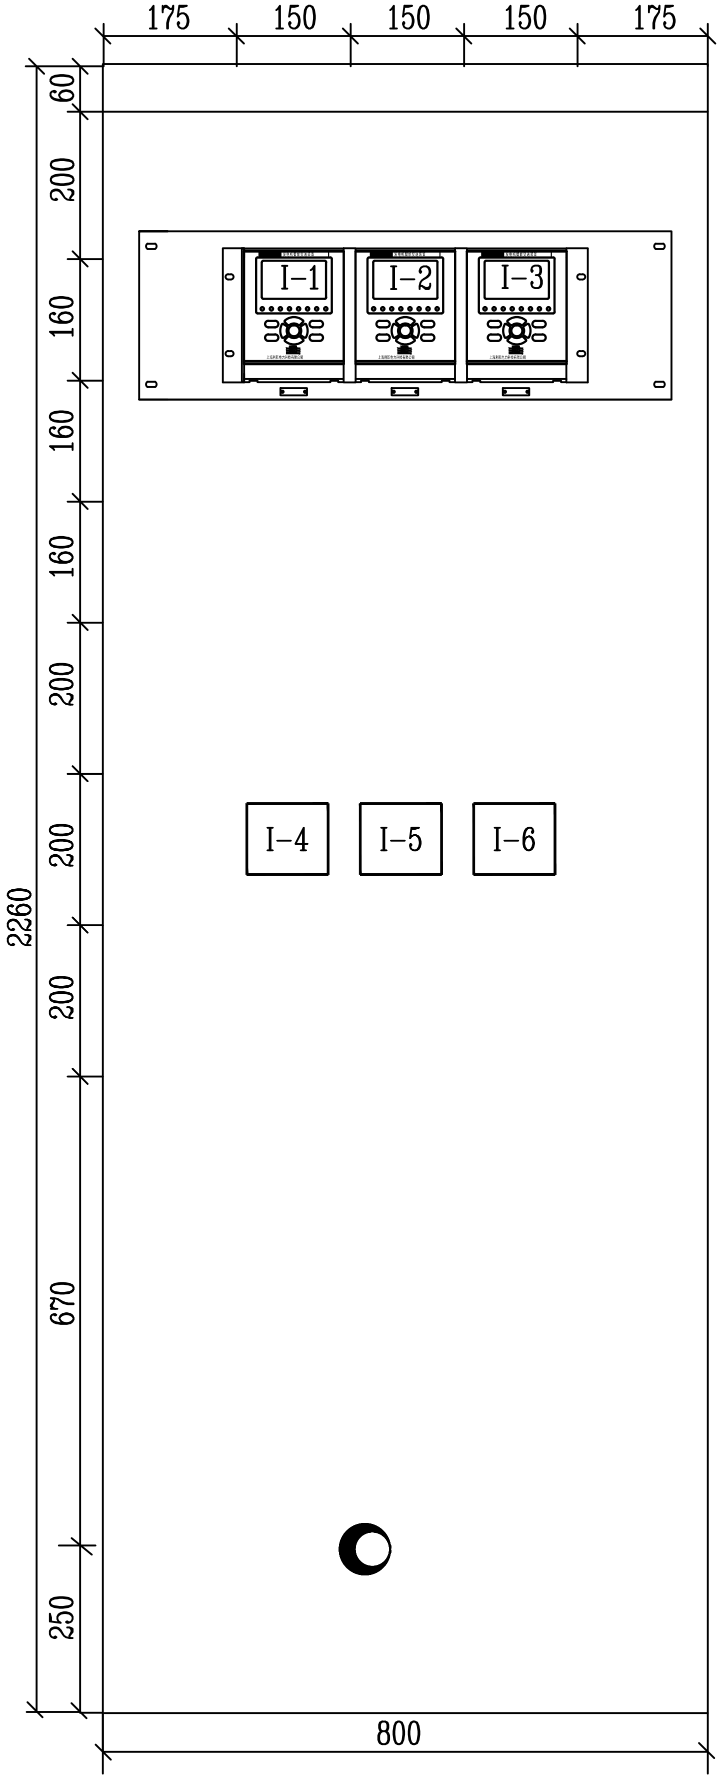

设备表

编号	符号	名称	型式及技术特性	数量	备注
安装单位I　发变组变送器					
I-1~3	1~3BPT	发电机智能变送装置	BPT9301 双电源 输出:8路4~20mA	3	10/0.1kV, 800/1A
I-4	1Af	三组合交流电流变送器	FPAX-A1-F1-P2-03 输出:4~20mA	1	800/1A
I-5	1HZf	频率变送器	FPF-F1-P2-013/B4 输出:4~12~20mA	1	
I-6	-QF1、-QF2	控制断路器	C65N-C10A/1P AC220V,10A,1P	2	屏后安装

屏体颜色：RAL7035　屏体门轴位置（面对屏体正面）：左　柜门型式：嵌入式　防护等级：IP42

0123456789AB

兴安盟金风科技蒸汽发电节能技术改造项目EPC工程总承包			工程	招标附图 设计阶段	图纸级别
批准		设计		机组变送器屏接线图	
审核		勘测			
		比例			
校核		日期		图号 D-03	版本

中国能源建设集团新疆电力设计院有限公司
CHINA ENERGY ENGINEERING GROUP XINJIANG ELECTRIC POWER DESIGN INSTITUTE CO., LTD.

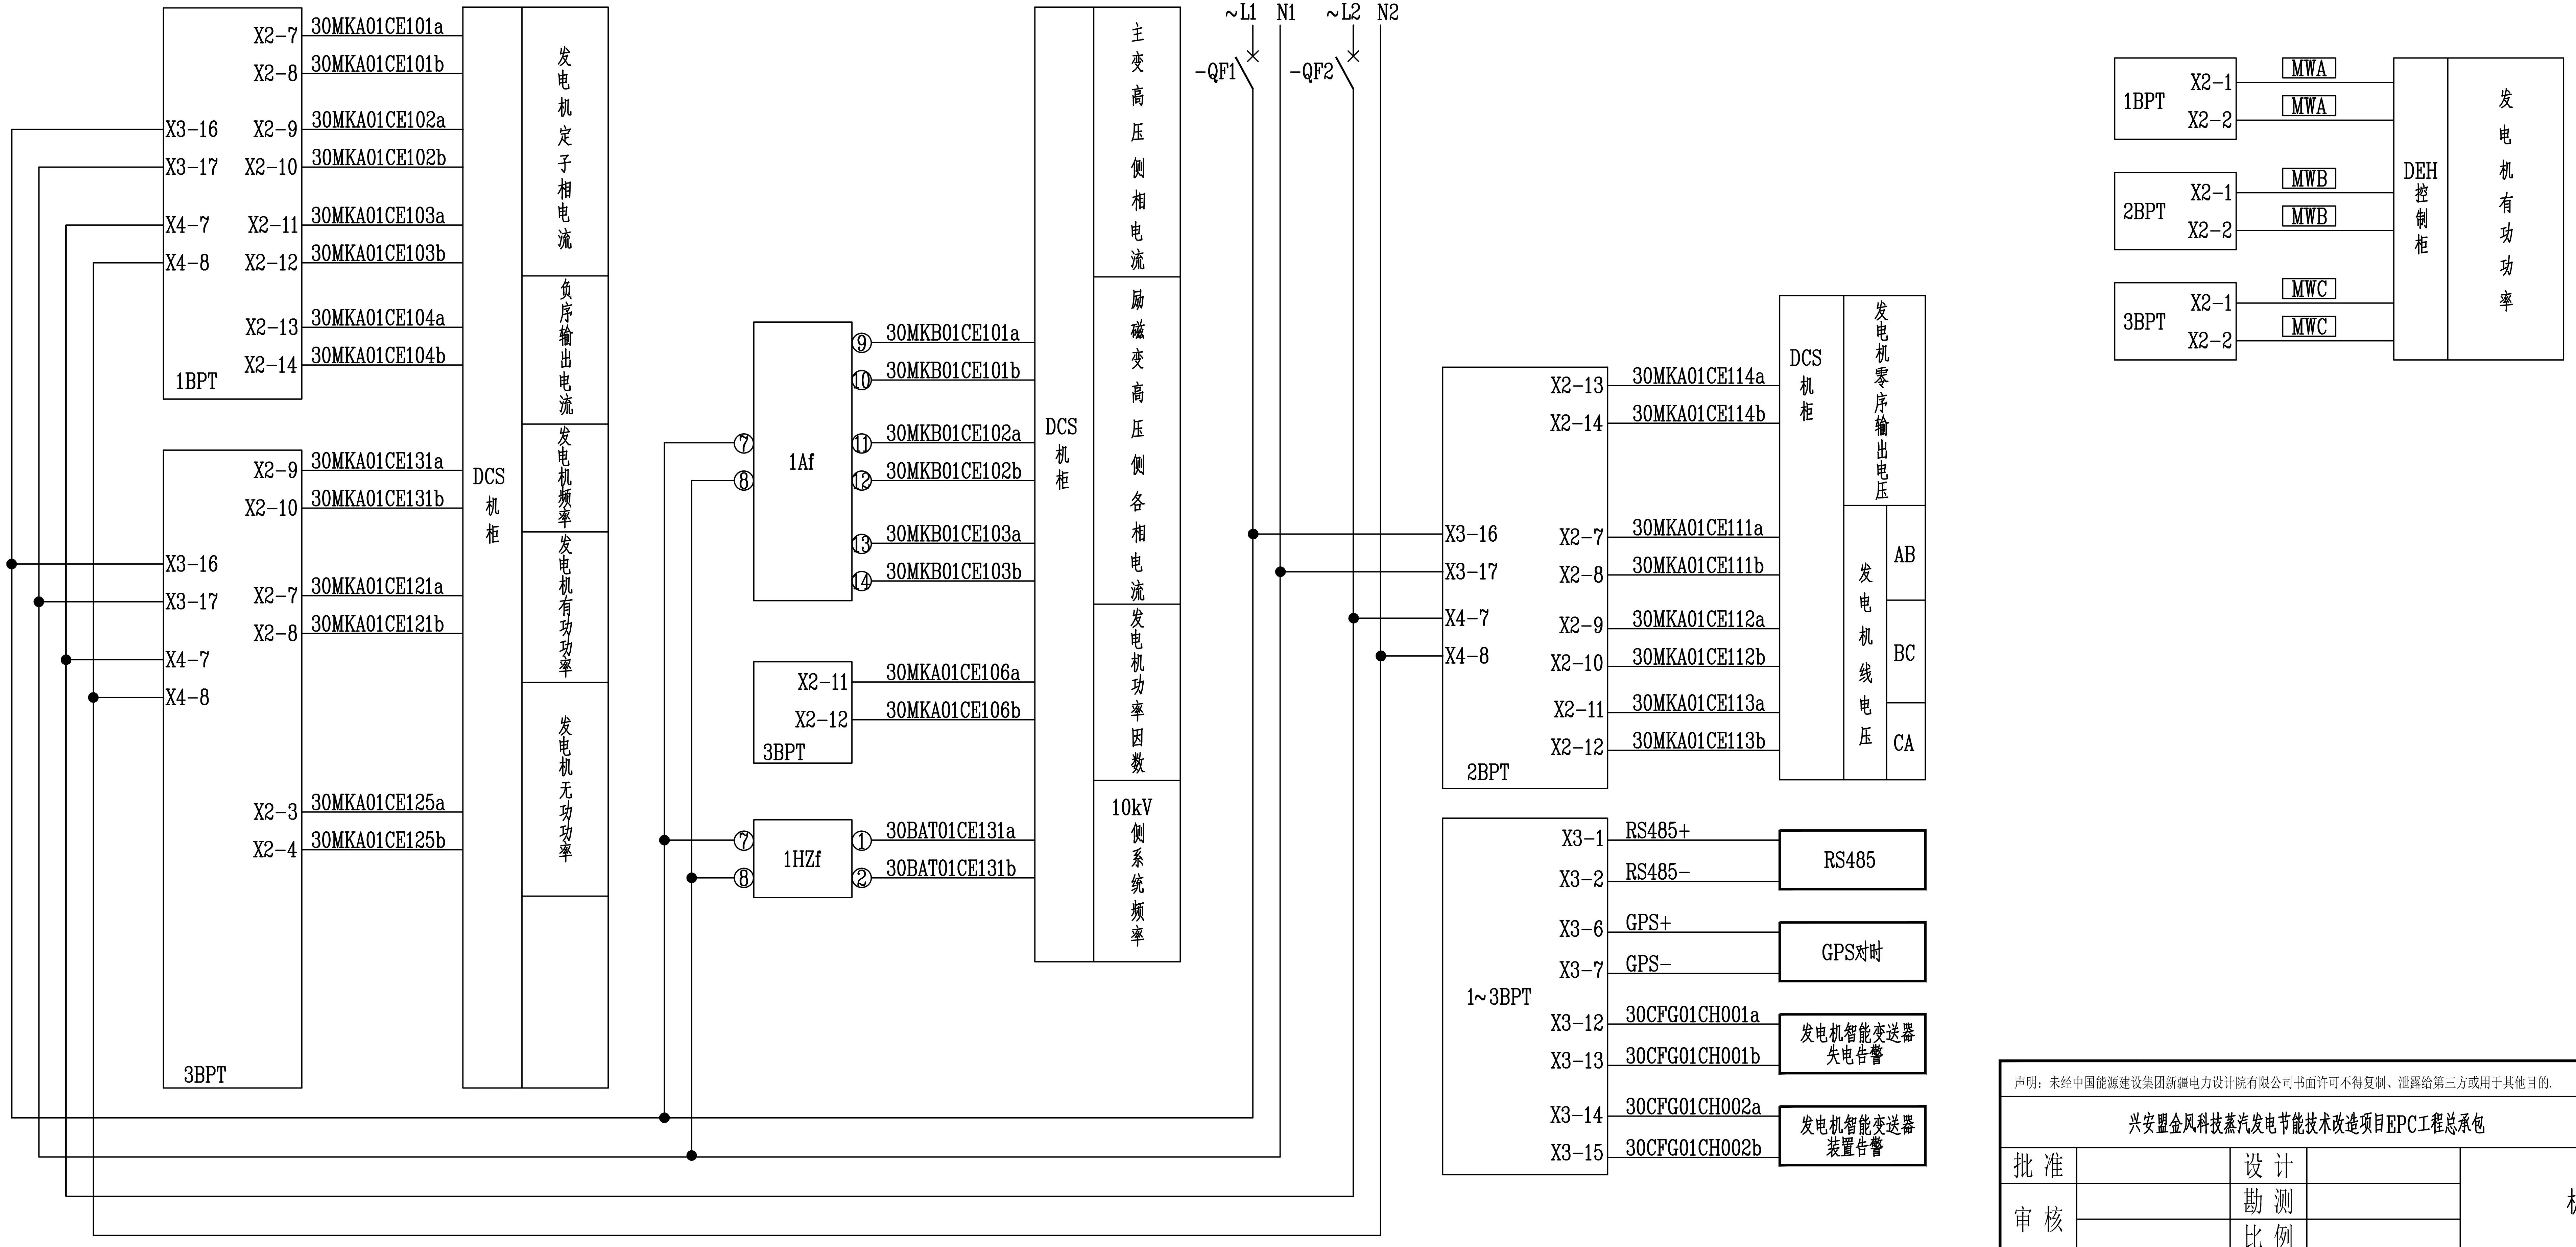

兴安盟金风科技蒸汽发电节能技术改造项目EPC工程总承包		工程	招标附图	设计阶段	图纸级别
批 准		设 计		机组变送器屏接线图	
审 核		勘 测			
		比 例			
校 核		日 期		图 号	D-03
					版本

中国能源建设集团新疆电力设计院有限公司
CHINA ENERGY ENGINEERING GROUP XINJIANG ELECTRIC POWER DESIGN INSTITUTE CO., LTD.